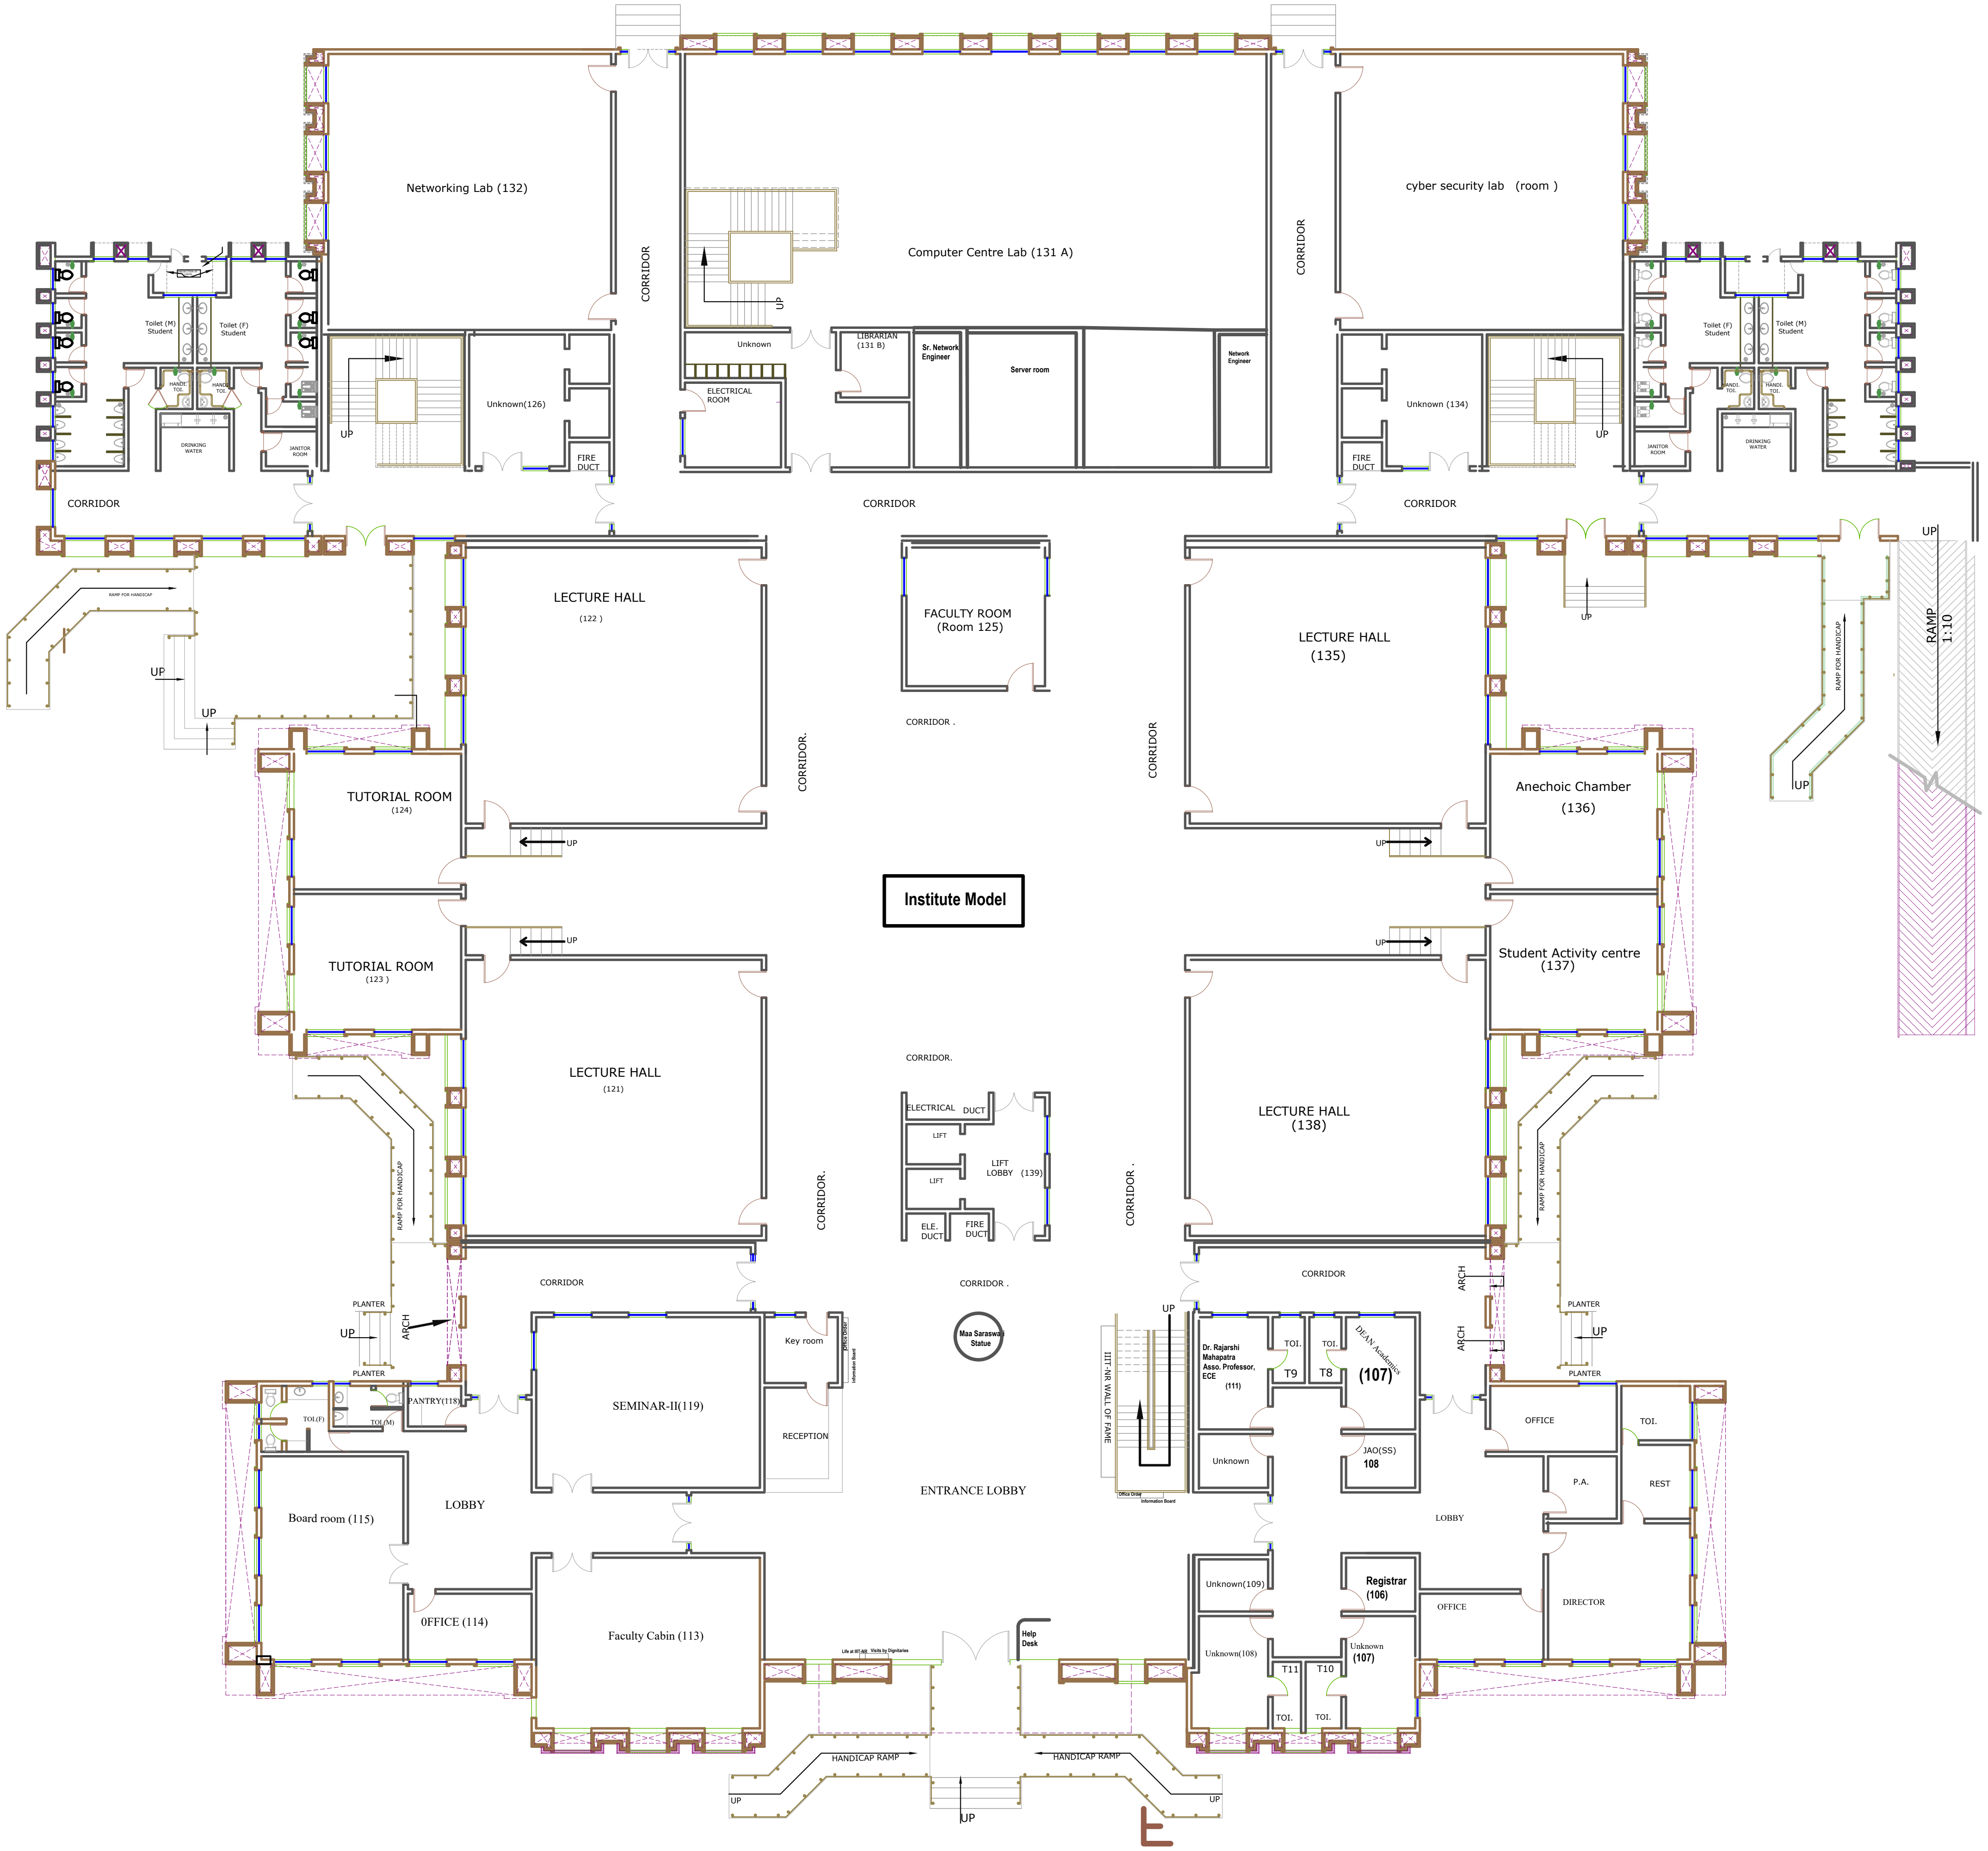
Networking Lab (132)
CORRIDOR
Computer Centre Lab (131 A)
UP
CORRIDOR
cyber security lab (room)
Toilet (M) Student
Toilet (F) Student
PROJECTION AT LINTEL
HANDI. TOI.
HANDI. TOI.
DRINKING WATER
JANITOR ROOM
UP
Unknown(126)
FIRE DUCT
Unknown
ELECTRICAL ROOM
LIBRARIAN (131 B)
Sr. Network Engineer
Server room
Network Engineer
Unknown (134)
FIRE DUCT
UP
Toilet (F) Student
Toilet (M) Student
HANDI. TOI.
HANDI. TOI.
JANITOR ROOM
DRINKING WATER
CORRIDOR
CORRIDOR
CORRIDOR
RAMP FOR HANDICAP
UP
UP
LECTURE HALL (122)
FACULTY ROOM (Room 125)
CORRIDOR .
LECTURE HALL (135)
UP
UP
RAMP FOR HANDICAP
RAMP 1:10
UP
UP
CORRIDOR.
CORRIDOR
TUTORIAL ROOM (124)
UP
Anechoic Chamber (136)
UP
Institute Model
UP
TUTORIAL ROOM (123)
UP
Student Activity centre (137)
LECTURE HALL (121)
CORRIDOR.
ELECTRICAL DUCT
LIFT
LIFT
LIFT LOBBY (139)
ELE. DUCT
FIRE DUCT
LECTURE HALL (138)
RAMP FOR HANDICAP
CORRIDOR.
CORRIDOR .
RAMP FOR HANDICAP
CORRIDOR
CORRIDOR .
CORRIDOR
ARCH
ARCH
PLANTER
UP
ARCH
PLANTER
PLANTER
UP
PLANTER
TOI.(F)
TOI.(M)
PANTRY(118)
SEMINAR-II(119)
Key room
Office Order
Information Board
RECEPTION
Maa Saraswati Statue
UP
IIIT-NR WALL OF FAME
Office Order
Information Board
Dr. Rajarshi Mahapatra Asso. Professor, ECE (111)
TOI.
TOI.
T9
T8
DEAN Academics
(107)
Unknown
JAO(SS) 108
OFFICE
TOI.
P.A.
REST
Board room (115)
LOBBY
ENTRANCE LOBBY
LOBBY
0FFICE (114)
Faculty Cabin (113)
Unknown(109)
Registrar (106)
OFFICE
DIRECTOR
Unknown(108)
Unknown (107)
Help Desk
Life at IIIT-NR
Visits by Dignitaries
T11
T10
TOI.
TOI.
HANDICAP RAMP
HANDICAP RAMP
UP
UP
UP